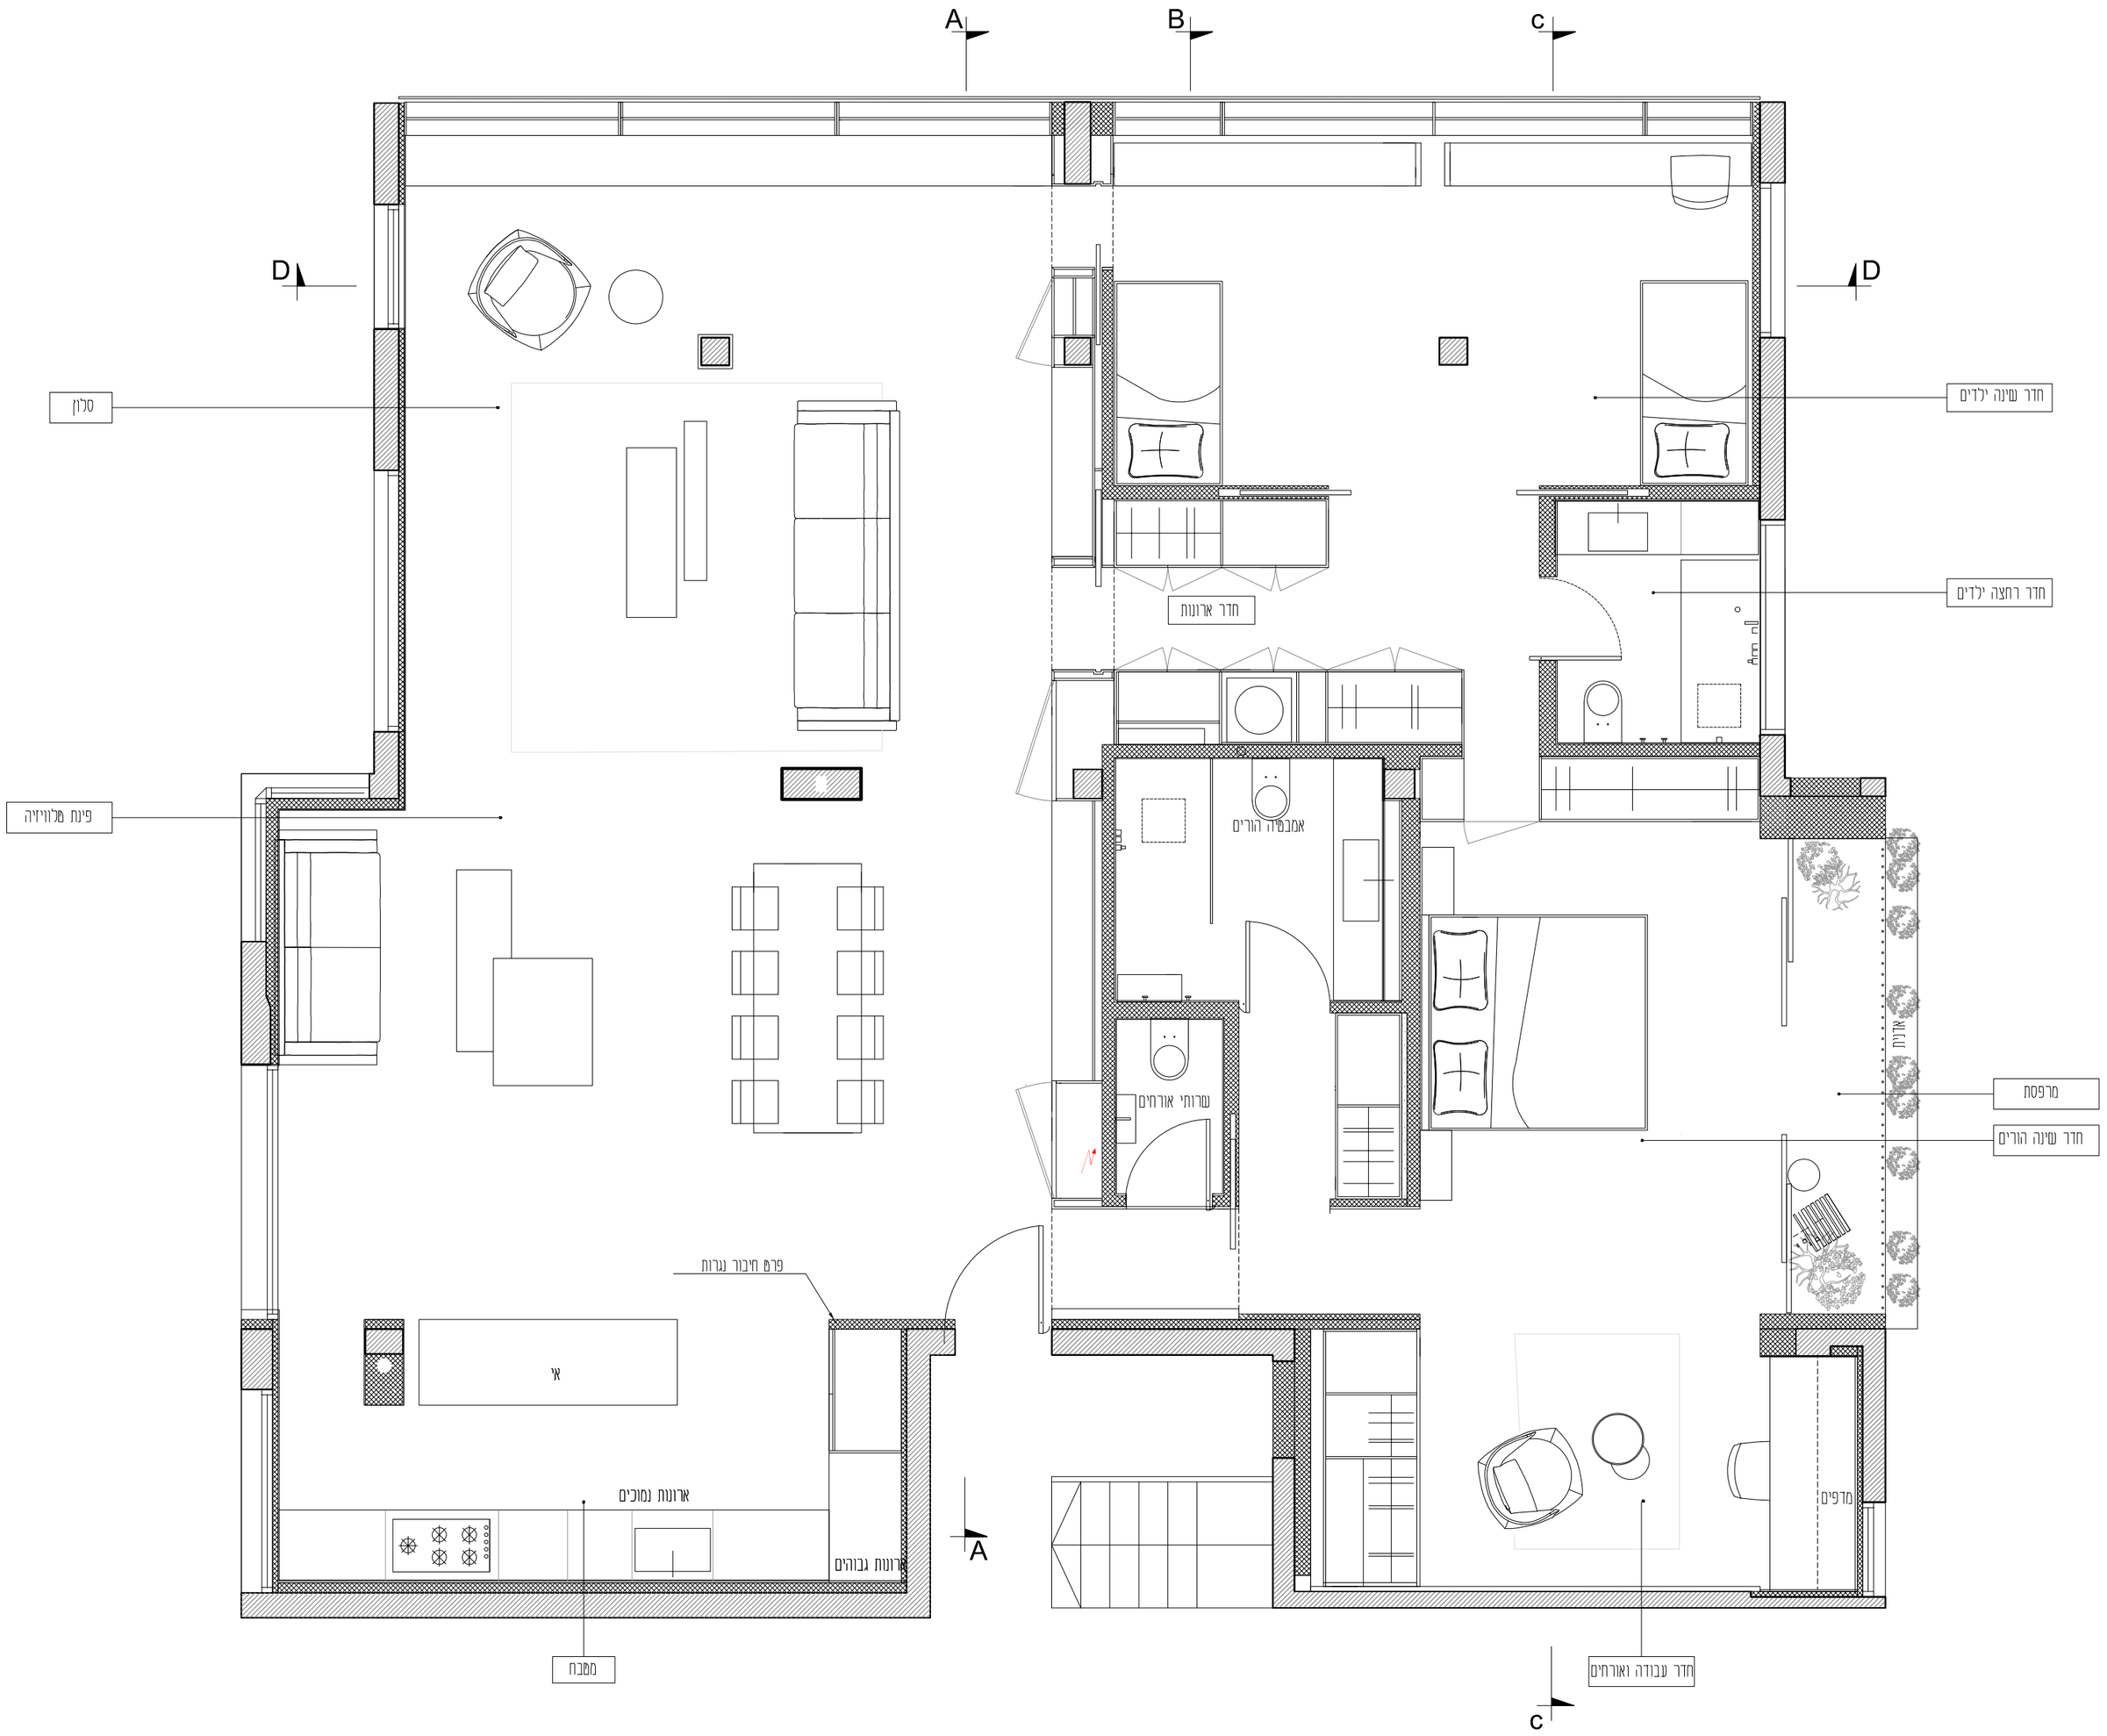

עדכונים : מס:	תאריך:	תאור:
01	06.03.18	
02	21.03.18	פירוט תכנית
03	12.07.18	העמדה חדשה
04	24.07.18	עדכון העמדה וקונסטרוקציה
05	29.08.18	עדכון
06	03.10.18	שינויים בתכנון בנייה
07	24.10.18	שינויים בתכנון בעקבות תכנון חשמל

עדכונים : מס:	תאריך:	תאור:
08	26.11.18	הורדת גברות 04
02	27.11.18	שינוי בחדר שינה ילדים
03	19.12.18	עדכונים בגברות
04	08.01.18	עדכונים בגברות
05	20.06.18	עדכונים בהעמדת ריהוט
06	30.07.18	עדכונים בהעמדת ריהוט- לבקשת מלי
07		

תפוצה:	תאריך:
אדריכל	
קבלן	
לקוח	
מ"מ	
מהנדס	
י. אינס	
י. חשמל	
י. תאורה	

מהדורה: 01

ברנוביץ גולדברג אדריכלים
אלפסי 32 ת"א טל-פקס: 03-5671747

תאריך: 30.07.19

גליון מס: Pines_Plan_Furn

קנ"מ: 1:50

שם הפרוייקט : Project Name
בית משפחת פינס- רמברנט 22

שם השרטוט : Drawing Name
תכנית העמדה

Review	Tender	Build
לעיון	למכרז	לביצוע

ההכניות הן רכושו של האדריכל ולא יישמה בהן כל שימוש ללא אישור מפורש של האדריכל . הקבלן אחראי לסידור ועליו לדווח לאדריכל על כל אי התאמה בין הסידורים הביוטמת והמצב בשטח עם להתייחס אך ורק לסידורים המפורטים ואין לסדור ישירות מהתכנית

BARANOWITZ & GOLDBERG
A R C H I T E C T S